


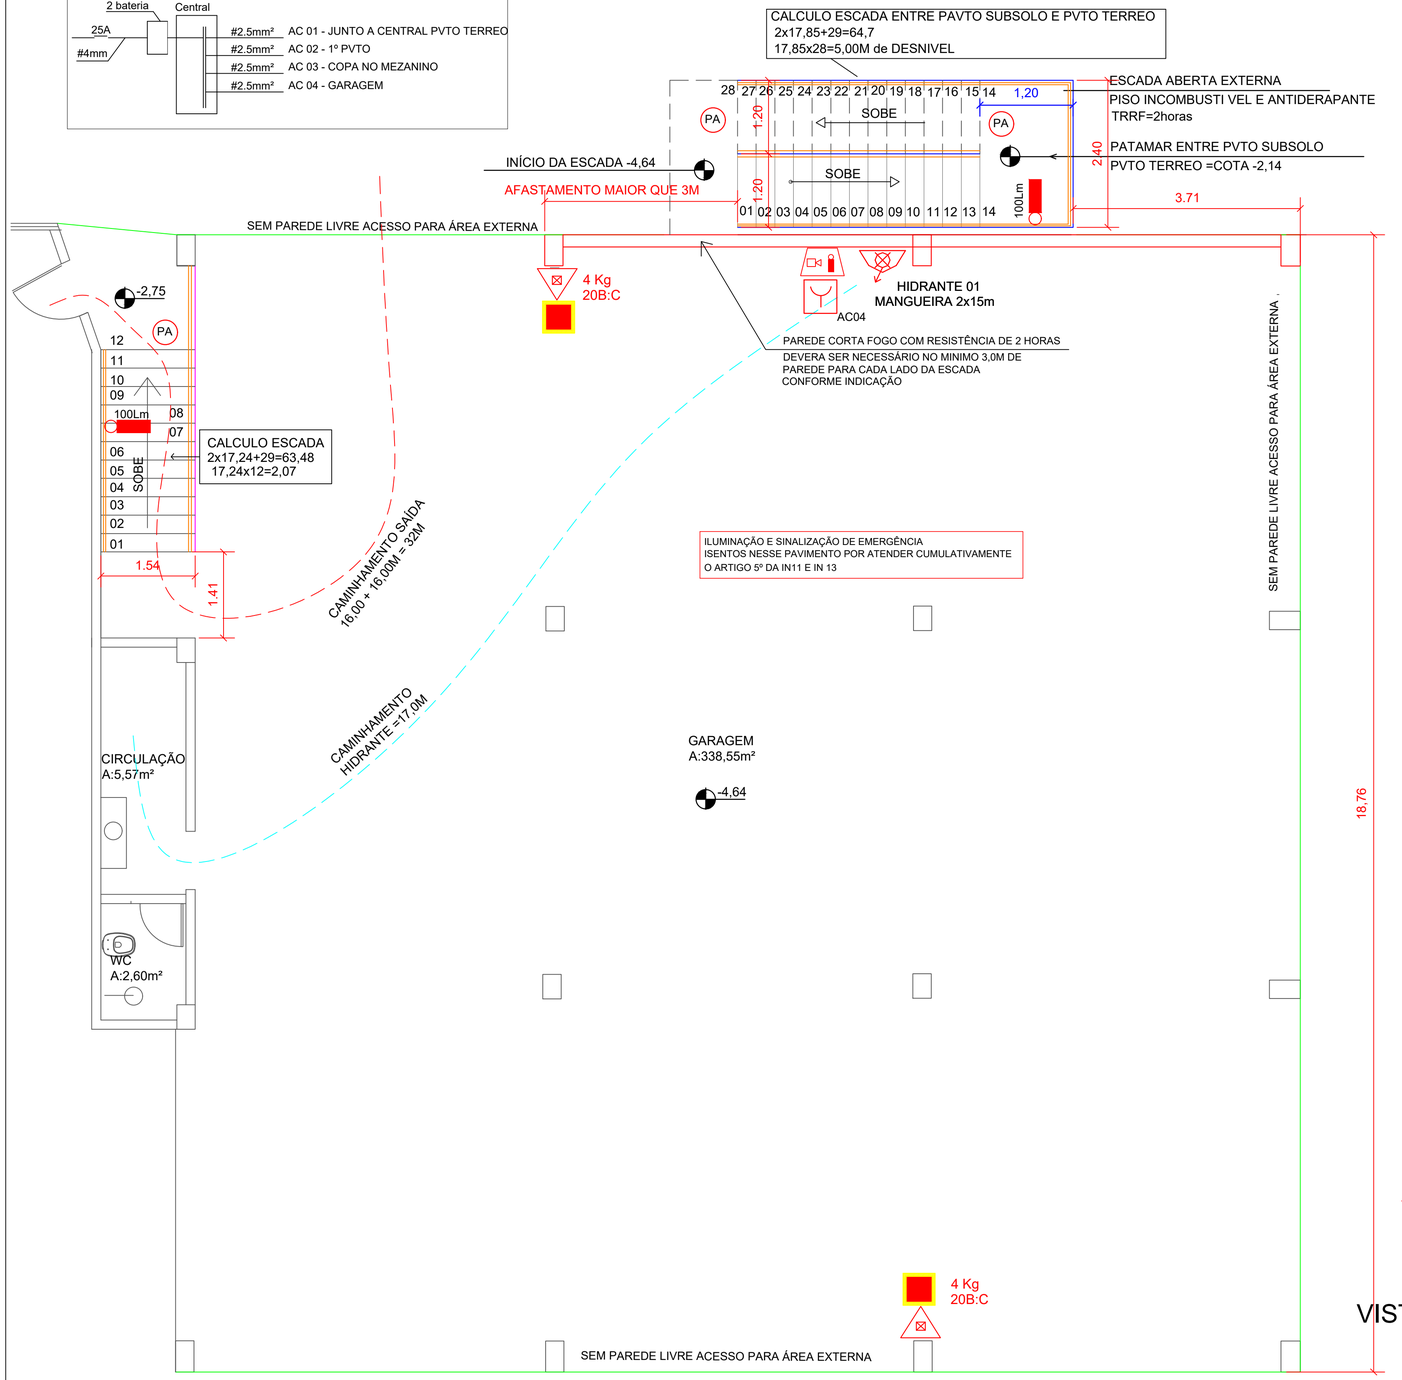

PLANTA BAIXA GARAGEM SUBSOLO (COTA PAVIMENTO -4,64M)

ÁREA DO PAVIMENTO :355,30M2

ESC 1/50

MATERIAIS DE REVESTIMENTOS E ACABAMENTOS

GARAGEM PVTO COTA -4,64M	PISO		PAREDE E DIVISÓRIAS (sem gotejamento flamejante)		TETO E FORRO (sem gotejamento)		COBERTURA (face superior)		FACHADA	
	Material Adotado	Classe Adotado	Material adotado	Classe Adotado	Material adotado	Classe Adotado	Material adotado	Classe Adotado	Material adotado	Classe Adotado
Garagem	Concreto	Classe I	Reboco	Classe I	Laje	Classe I	Laje	Classe I	Aberto	
WC	Cerâmico	Classe I	Cerâmico	Classe I	Laje	Classe I	Laje	Classe I	Reboco	Classe I

NOTAS:


O MEMORIAL FAZ PARTE DO PROJETO. A TABELA DE CLASSIFICAÇÃO E MATERIAIS DE ACABAMENTO, E O RESTANTE DAS INFORMAÇÕES E DIMENSIONAMENTOS REFERENTES A ESTE PROJETO, ENCONTRAM-SE NO MEMORIAL DESCRITIVO.

DEVER SER PREVISTO CIRCUITO ELÉTRICO PARA SIE E SAL, COM DISJUNTOR DEVIDAMENTE IDENTIFICADO, INDEPENDENTEMENTE DO TIPO DE FONTE DE ENERGIA UTILIZADO, DEVENDO O SIE E SAL TER AUTONOMIA MINIMA DE 2 HORAS, GARANTINDO O NÍVEL DE ILUMINAMENTO. O SIE DEVE POSSUIR UMA TOMADA EXCLUSIVA PARA CADA BLOCO.

NAS ROTAS DE FUGA HORIZONTAIS E VERTICAIS (CIRCULAÇÃO, CORREDORES, HALL, ESCADAS, RAMPAS, ETC), A ILUMINAÇÃO CONVENCIONAL DESTES AMBIENTES DEVE TER ACIONAMENTO AUTOMÁTICO (POR EXEMPLO COM O USO DE SENROR DE PRESENÇA).


O PROJETO PREVENTIVO CONTRA INCÊNCIO, ATENDE A IN 19, NORMATIVA TÉCNICA DE INSTALAÇÕES ELÉTRICAS DE BAIXA TENSÃO.

QUADRO DE ÁREAS			
	Área aprovada	Ampliação	Total
Pvto Garagem (sub solo)	342,71	12,59	355,3
Pvto mezanino (sub solo)		71,7	71,7
1º Pvto	568,37		568,37
2º Pvto	568,37		568,37
TOTAL	1479,45	84,29	**1563,74**
Ampliação	5,70%		

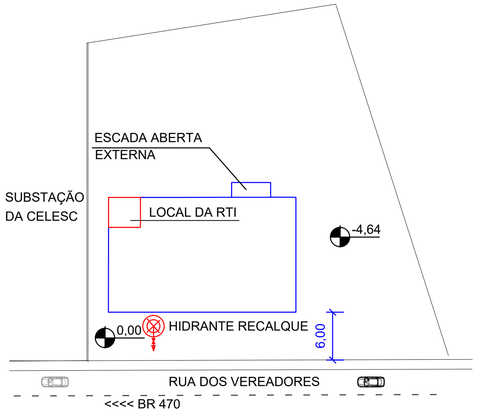

PLANTA DE SITUAÇÃO

SEM ESCALA

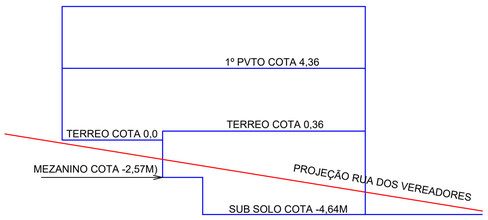

VISTA FRONTAL EXPLICATICA DOS NIVEIS

LEGENDA

- 4 Kg 20B:C — EXTINTOR PORTÁTIL COM CARGA DE PÓ BC 4KG 20-B:C
- PINTURA DE PISO
- 100Lm — PONTO DE ILUMINAÇÃO DE EMERGÊNCIA 100 LUMENS
- 1200 Lm — PONTO DE ILUMINAÇÃO DE EMERGÊNCIA 1200 LUMENS
- SAÍDA — PLACA FOTOLUMINECENTE COM INDICAÇÃO DE SAÍDA DIMENSÕES DA PLACA JUNTO A INDICAÇÃO DE SAÍDA NA PLANTA
- PLACA FOTOLUMINECENTE COM INDICAÇÃO SO SENTIDO DA SAÍDA DIMENSÕES DA PLACA JUNTO A INDICAÇÃO DE SAÍDA NA PLANTA
- HIDRANTE DE SIMPLES PERMANECE CONFORME PROJETO PREVIAMENTE APROVADO
- REGISTRO DE RECALQUE COM VÁLVULA DE RETENÇÃO PERMANECE CONFORME PROJETO PREVIAMENTE APROVADO
- CENTRAL DO SISTEMA DE DETECÇÃO E ALARME PERMANECE CONFORME PROJETO PREVIAMENTE APROVADO
- AVISADOR SONORO E VISUAL COM SIRENE PERMANECE CONFORME PROJETO PREVIAMENTE APROVADO
- ACIONADOR MANUAL DO SISTEMA DE DETECÇÃO E ALARME PERMANECE CONFORME PROJETO PREVIAMENTE APROVADO
- PA — PISO ANTIDERAPANTE
- SEM PAREDE LIVRE ACESSO PARA ÁREA EXTERNA
- GUARDA CORPO DA ESCADA EXTERNA ALTURA MÍNIMA DE 1,30m
- GUARDA CORPO ALTURA MÍNIMA DE 1,10m
- CORRIMÃO NA ESCADA ALTURA ENTRE 0,8 E 0,92m
- CORRIMÃO DUAS ALTURAS NA RAMPA
- LINHA COM INDICAÇÃO DE CAMINHAMENTOS DIVERSOS
- LINHA COM INDICAÇÃO DO HIDRANTE
- LINHA INDICAÇÃO DE CAMINHAMENTOS DAS UNIDADES AUTÔNOMAS (ATÉ 10,0m)
- FITA FOTOLUMINESCENTE E FITAS ANTIDERRAPANTES
- PLACA DE ADVERTENCIA (DEGRAU IRREGULAR)

NOTAS:

CAMINHAMENTO MÁXIMO DO PAVIMENTO DESCARGA, SAÍDA UNICA = 40,0M

OCUPAÇÃO DE ESCRITÓRIO (D1)

SISTEMA DE ALARME E DETECÇÃO E SISTEMA HIDRAULICO PREVENTIVO PERMANECEM CONFORME PROJETO PREVIAMENTE APROVADO CONFORME PROTOCOLO 26288 - RE 6269

CARIMBOS:

ARIEL ANDRE MASSON
ENGENHEIRO CIVIL
CREA-SC 126637-3
47-988231636

PROPRIETÁRIO: Sooltech Desenvolvimento e Comércio de Sistemas Ltda — CNPJ: 80.090.244/0001-41

OBRA: EDIFICAÇÃO COM OCUPAÇÃO DE ESCRITÓRIO

ENDEREÇO: RUA DOS VEREADORES - BAIRRO ITOUPAVA - RIO DO SUL/SC

CONTEÚDO: PLANTA BAIXA GARAGEM SUBSOLO (COTA PAVIMENTO -4,64M) PLANTA DE SITUAÇÃO LEGENDA

DESENHO: LUCIANO R. KRUGER
ÁREA: 1.563,74 m²
ESCALA: 1/50
DATA: 05/05/2023
FOLHA: 01 / 05

RESPONSÁVEL TÉCNICO: ARIEL ANDRÉ MASSON CREA-SC: 126637-3

Assinado de forma digital por ARIEL ANDRE MASSON:06486173981 Dados: 2024.05.14 10:21:23 -03'00'

PROPRIETÁRIO:

PROJETO: PREVENTIVO

É vedada a reprodução e/ou utilização do projeto sem a autorização do autor Lei nº 5.988/73 - Direito Autoral