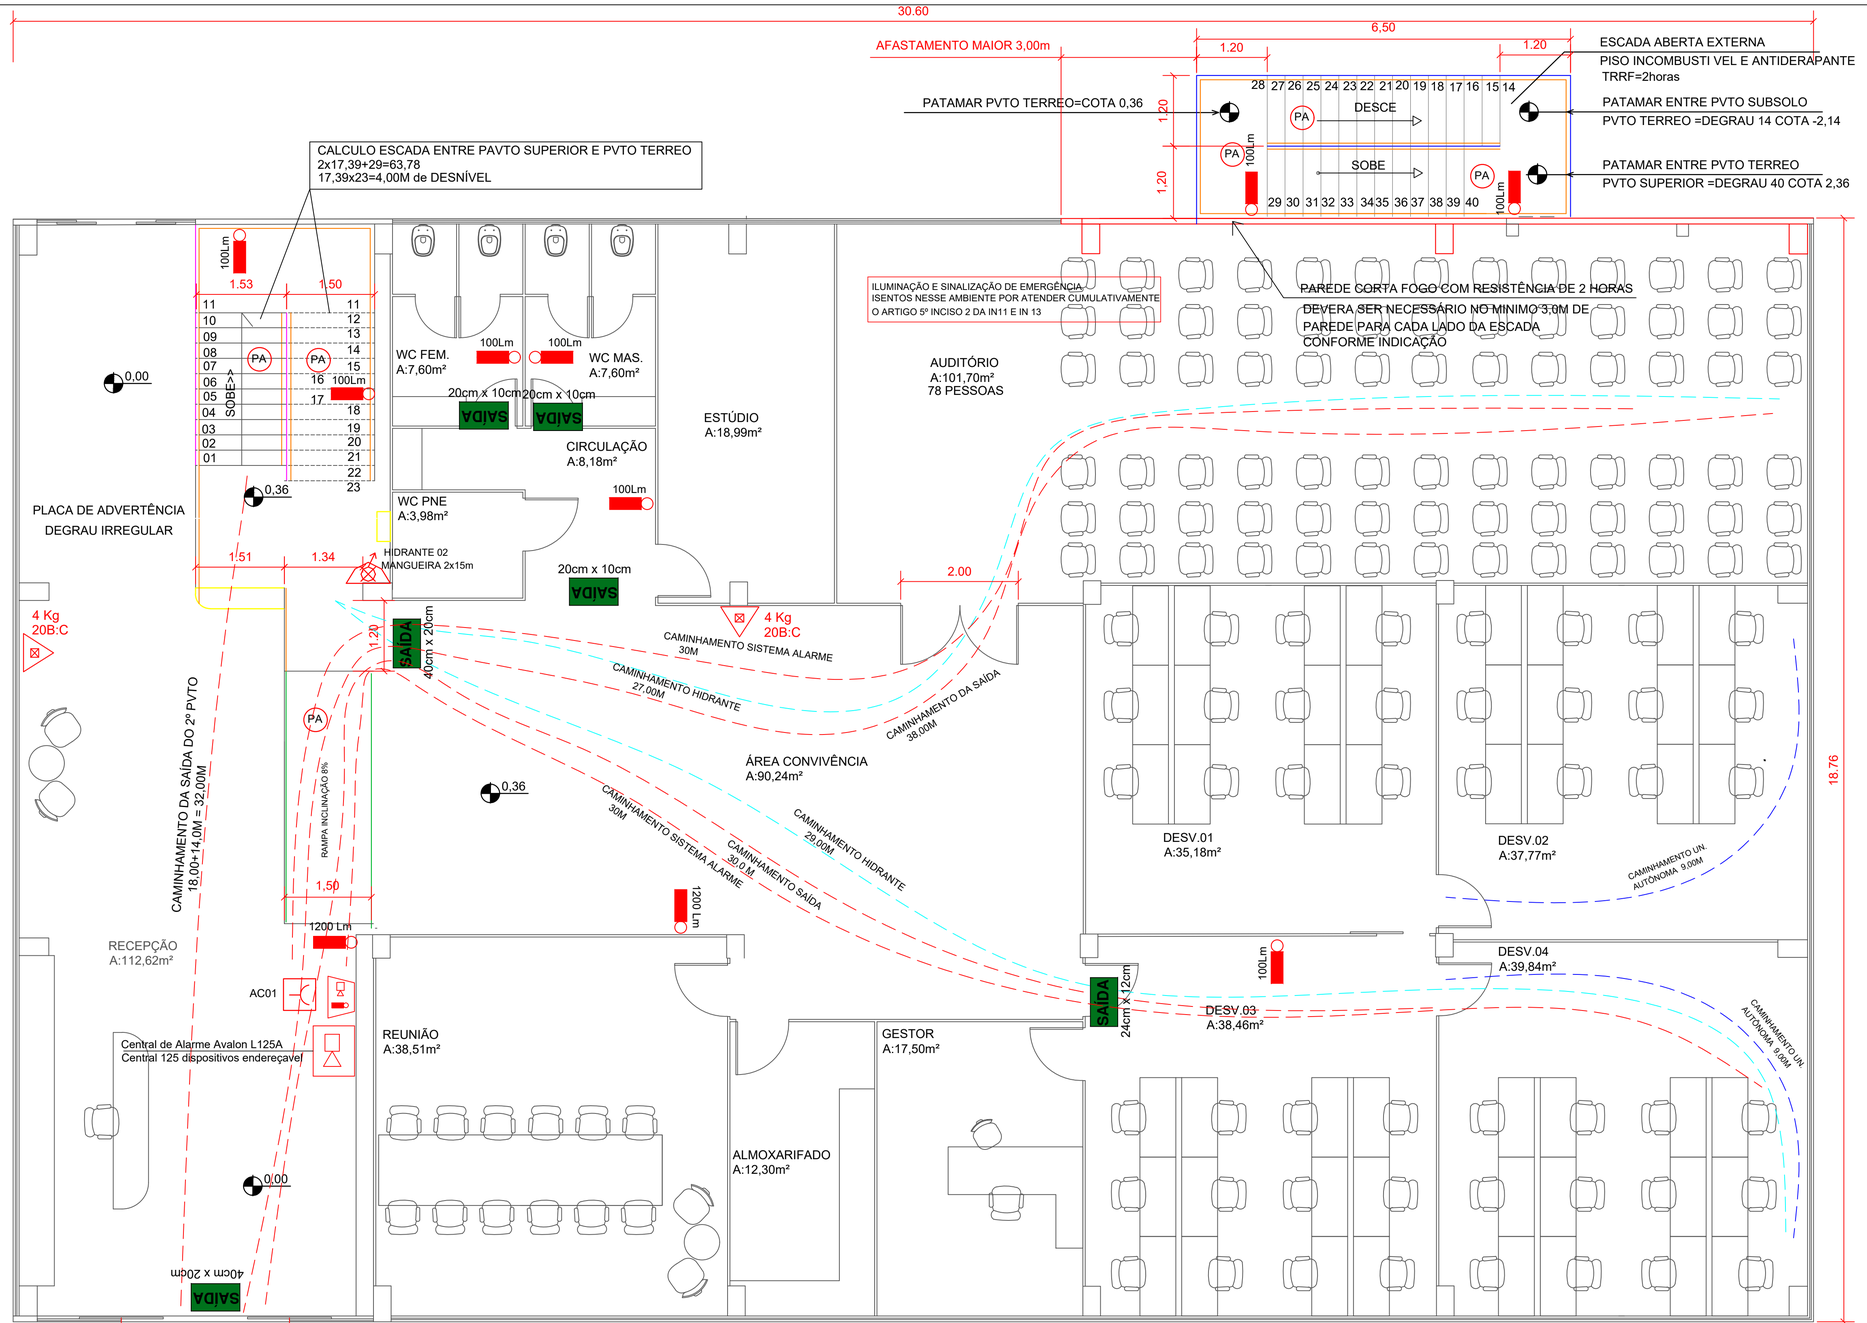


PLANTA BAIXA TÉRREO (COTA PAVIMENTO 0,00 e 0,36)

ÁREA DO PAVIMENTO :568,37M2

ESC 1/50

LEGENDA

- 4 Kg 20B:C — EXTINTOR PORTÁTIL COM CARGA DE PÓ BC 4KG 20-B:C
- PINTURA DE PISO
- 100Lm — PONTO DE ILUMINAÇÃO DE EMERGÊNCIA 100 LUMENS
- 1200 Lm — PONTO DE ILUMINAÇÃO DE EMERGÊNCIA 1200 LUMENS
- SAÍDA — PLACA FOTOLUMINECENTE COM INDICAÇÃO DE SAÍDA DIMENSÕES DA PLACA JUNTO A INDICAÇÃO DE SAÍDA NA PLANTA
- PLACA FOTOLUMINECENTE COM INDICAÇÃO SO SENTIDO DA SAÍDA DIMENSÕES DA PLACA JUNTO A INDICAÇÃO DE SAÍDA NA PLANTA
- HIDRANTE DE SIMPLES PERMANECE CONFORME PROJETO PREVIAMENTE APROVADO
- REGISTRO DE RECALQUE COM VÁLVULA DE RETENÇÃO PERMANECE CONFORME PROJETO PREVIAMENTE APROVADO
- CENTRAL DO SISTEMA DE DETECÇÃO E ALARME PERMANECE CONFORME PROJETO PREVIAMENTE APROVADO
- AVISADOR SONORO E VISUAL COM SIRENE PERMANECE CONFORME PROJETO PREVIAMENTE APROVADO
- ACIONADOR MANUAL DO SISTEMA DE DETECÇÃO E ALARME PERMANECE CONFORME PROJETO PREVIAMENTE APROVADO
- PA — PISO ANTIDERAPANTE
- SEM PAREDE LIVRE ACESSO PARA ÁREA EXTERNA
- GUARDA CORPO DA ESCADA EXTERNA ALTURA MÍNIMA DE 1,30m
- GUARDA CORPO ALTURA MÍNIMA DE 1,10m
- CORRIMÃO NA ESCADA ALTURA ENTRE 0,8 E 0,92m
- CORRIMÃO DUAS ALTURAS NA RAMPA
- LINHA COM INDICAÇÃO DE CAMINHAMENTOS DIVERSOS
- LINHA COM INDICAÇÃO DO HIDRANTE
- LINHA INDICAÇÃO DE CAMINHAMENTOS DAS UNIDADES AUTÔNOMAS (ATÉ 10,0m)
- FITA FOTOLUMINESCENTE E FITAS ANTIDERRAPANTES
- PLACA DE ADVERTENCIA (DEGRAU IRREGULAR)

NOTAS:
CAMINHAMENTO MÁXIMO DO PAVIMENTO DESCARGA, SAÍDA UNICA = 40,0M

MATERIAIS DE REVESTIMENTOS E ACABAMENTOS

Pvto terreo	PISO		PAREDE E DIVISÓRIAS (sem gotejamento flamejante)		TETO E FORRO (sem gotejamento)		COBERTURA (face superior)		FACHADA	
	Material Adotado	Classe Adotado	Material adotado	Classe Adotado	Material adotado	Classe Adotado	Material adotado	Classe Adotado	Material adotado	Classe Adotado
Escada	Granito	Classe I	Reboco e Alvenaria	Classe I	Área Aberta	_____	Laje	Classe I	Pré moldado de concreto	Classe I
BWC	Cerâmico	Classe I	Cerâmico	Classe I	Laje	Classe I	Laje	Classe I	Pré moldado de concreto	Classe I
Recepção	Cerâmico	Classe I	Reboco e Alvenaria	Classe I	Laje	Classe I	Laje	Classe I	Pré moldado de concreto	Classe I
Salas	Vinílico	Classe IV-A	Reboco e Alvenaria	Classe I	Laje	Classe I	Laje	Classe I	Pré moldado de concreto	Classe I
Auditório	Carpete	Classe III-A	Reboco e Alvenaria	Classe I	Laje	Classe I	Laje	Classe I	Pré moldado de concreto	Classe I

CARIMBOS:

ARIEL ANDRE MASSON
ENGENHEIRO CIVIL
CREA-SC 126637-3
47-988231636

PROPRIETÁRIO: Soeltech Desenvolvimento e Comércio de Sistemas Ltda — CNPJ: 80.090.244/0001-41

OBRA: EDIFICAÇÃO COM OCUPAÇÃO DE ESCRITÓRIO

ENDEREÇO: RUA DOS VEREADORES - BAIRRO ITOUPAVA - RIO DO SUL/SC

CONTEÚDO: PLANTA BAIXA TÉRREO (COTA PAVIMENTO 0,00 e 0,36) LEGENDA

DESENHO: LUCIANO R. KRUGER
ÁREA: 1.563,74 m²
ESCALA: 1/50
DATA: 05/05/2023
FOLHA: 03 / 05

RESPONSÁVEL TÉCNICO: ARIEL ANDRÉ MASSON CREA-SC: 126637-3

PROPRIETÁRIO:

PROJETO: PREVENTIVO

É vedada a reprodução e/ou utilização do projeto sem a autorização do autor Lei nº 5.988/73 - Direito Autoral