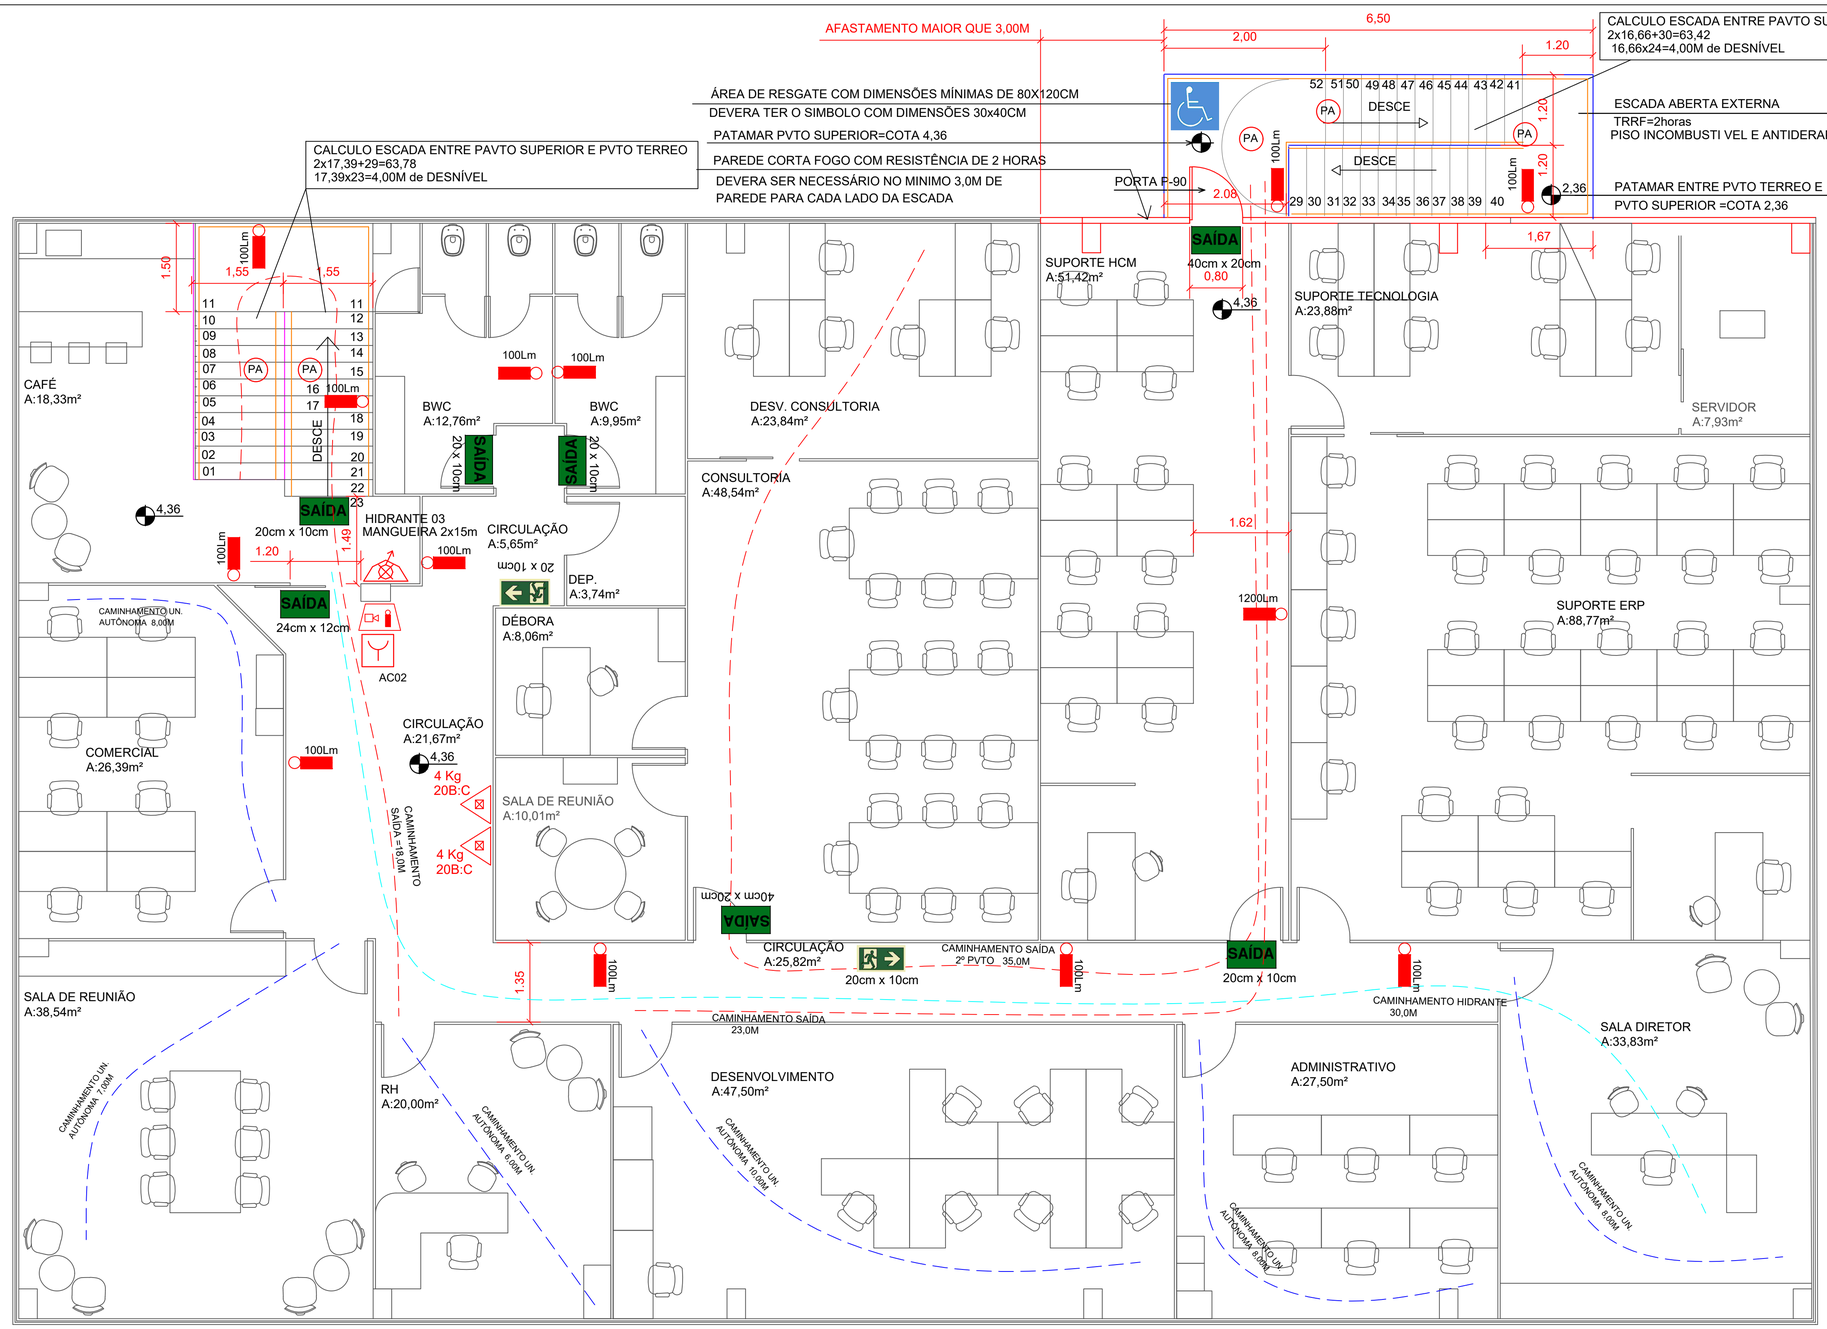


LEGENDA

- 4 Kg 20B:C — EXTINTOR PORTÁTIL COM CARGA DE PÓ BC 4KG 20-B:C
- PINTURA DE PISO
- 100Lm — PONTO DE ILUMINAÇÃO DE EMERGÊNCIA 100 LUMENS
- 1200 Lm — PONTO DE ILUMINAÇÃO DE EMERGÊNCIA 1200 LUMENS
- SAÍDA — PLACA FOTOLUMINECENTE COM INDICAÇÃO DE SAÍDA DIMENSÕES DA PLACA JUNTO A INDICAÇÃO DE SAÍDA NA PLANTA
- PLACA FOTOLUMINECENTE COM INDICAÇÃO SO SENTIDO DA SAÍDA DIMENSÕES DA PLACA JUNTO A INDICAÇÃO DE SAÍDA NA PLANTA
- HIDRANTE DE SIMPLES PERMANECE CONFORME PROJETO PREVIAMENTE APROVADO
- REGISTRO DE RECALQUE COM VÁLVULA DE RETENÇÃO PERMANECE CONFORME PROJETO PREVIAMENTE APROVADO
- CENTRAL DO SISTEMA DE DETECÇÃO E ALARME PERMANECE CONFORME PROJETO PREVIAMENTE APROVADO
- AVISADOR SONORO E VISUAL COM SIRENE PERMANECE CONFORME PROJETO PREVIAMENTE APROVADO
- ACIONADOR MANUAL DO SISTEMA DE DETECÇÃO E ALARME PERMANECE CONFORME PROJETO PREVIAMENTE APROVADO
- PA — PISO ANTIDERAPANTE
- SEM PAREDE LIVRE ACESSO PARA ÁREA EXTERNA
- GUARDA CORPO DA ESCADA EXTERNA ALTURA MÍNIMA DE 1,30m
- GUARDA CORPO ALTURA MÍNIMA DE 1,10m
- CORRIMÃO NA ESCADA ALTURA ENTRE 0,8 E 0,92m
- CORRIMÃO DUAS ALTURAS NA RAMPA
- LINHA COM INDICAÇÃO DE CAMINHAMENTOS DIVERSOS
- LINHA COM INDICAÇÃO DO HIDRANTE
- LINHA INDICAÇÃO DE CAMINHAMENTOS DAS UNIDADES AUTÔNOMAS (ATÉ 10,0m)
- FITA FOTOLUMINESCENTE E FITAS ANTIDERRAPANTES
- PLACA DE ADVERTENCIA (DEGRAU IRREGULAR)

NOTAS:
CAMINHAMENTO MÁXIMO DO PISO ELEVADO,MAIS DE UMA SAÍDA = 40,0M

PLANTA BAIXA 1º PVTO (COTA PAVIMENTO 4,36M)

ÁREA DO PAVIMENTO :568,37M2
ESC 1/50

MATERIAIS DE REVESTIMENTOS E ACABAMENTOS

1º pvto	PISO		PAREDE E DIVISÓRIAS (sem gotejamento flamejante)		TETO E FORRO (sem gotejamento)		COBERTURA (face superior)		FACHADA	
	Material Adotado	Classe Adotado	Material adotado	Classe Adotado	Material adotado	Classe Adotado	Material adotado	Classe Adotado	Material adotado	Classe Adotado
Salas	Vinílico	Classe IV-A	Pré moldado de concreto; Vidro; Gesso acartonado.	Classe I	Forro de Fibra Mineral	Classe II-A	Telha Metálica	Classe I	Pré moldado de concreto	Classe I
WC	Cerâmico	Classe I	Cerâmico	Classe I	Forro de Fibra Mineral	Classe II-A	Telha Metálica	Classe I	Pré moldado de concreto	Classe I
Escada	Granito	Classe I	Reboco e Alvenaria	Classe I	Forro de Fibra Mineral	Classe II-A	Telha Metálica	Classe I	Pré moldado de concreto	Classe I

CARIMBOS:

ARIEL ANDRE MASSON
ENGENHEIRO CIVIL
CREA-SC 126637-3
47-988231636

PROPRIETÁRIO: Soeltech Desenvolvimento e Comércio de Sistemas Ltda — CNPJ: 80.090.244/0001-41
OBRA: EDIFICAÇÃO COM OCUPAÇÃO DE ESCRITÓRIO
ENDEREÇO: RUA DOS VEREADORES - BAIRRO ITOUPAVA - RIO DO SUL/SC
CONTEÚDO: PLANTA BAIXA SUPERIOR (COTA PAVIMENTO 4,36M) / LEGENDA
DESENHO: LUCIANO R. KRUGER
ÁREA: 1.563,74 m²
ESCALA: 1/50
DATA: 05/05/2023
FOLHA: 04 / 05
RESPONSÁVEL TÉCNICO: ARIEL ANDRÉ MASSON CREA-SC: 126637-3
PROPRIETÁRIO:
PROJETO: PREVENTIVO

É vedada a reprodução e/ou utilização do projeto sem a autorização do autor Lei nº 5.988/73 - Direito Autoral