

DETALHE DO GUARDA CORPO E CORRIMÃO NA ESCADA

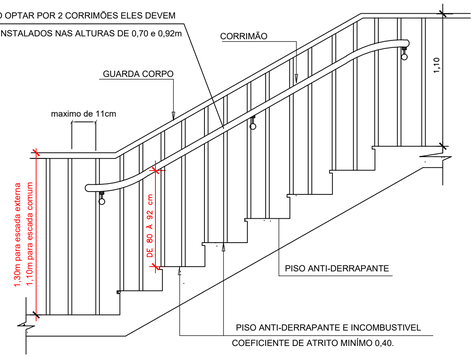

CORTE LONGITUDINAL ESQUEMÁTICO

CORTE TRANSVERSAL ESQUEMÁTICO

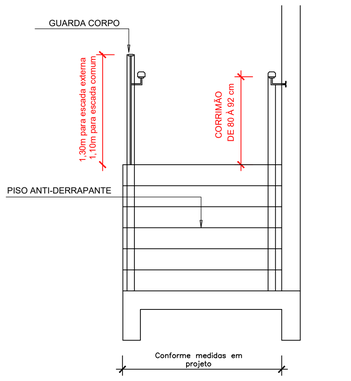


OBSERVAÇÃO


TODO ACABAMENTO E FINAIS DO CORRIMÃO DEVERÃO SER ARREDONDADOS E SEM O EFEITO DE GANCHO.
O COEFICIENTE DE ATRITO MINÍMO DO PISO DA ESCADA DEVERÁ SER SUPERIOR 0,40.

Quando for constuído por elementos vazados, deve impedir a passagem de uma esfera com 11 cm de diâmetro nas aberturas;


Não pode ser constuído por elementos que possibilitem a escalada por crianças, tais como: longarinas, grades, barras horizontais, etc.

DETALHE DO CORRIMÃO NA RAMPA

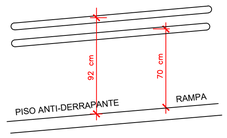


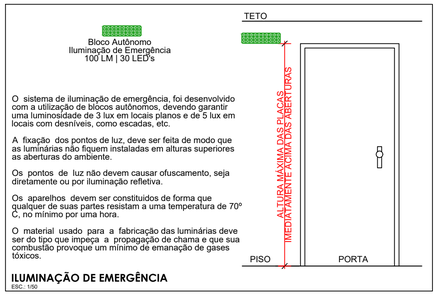

ILUMINAÇÃO DE EMERGÊNCIA
ESC. 1/50

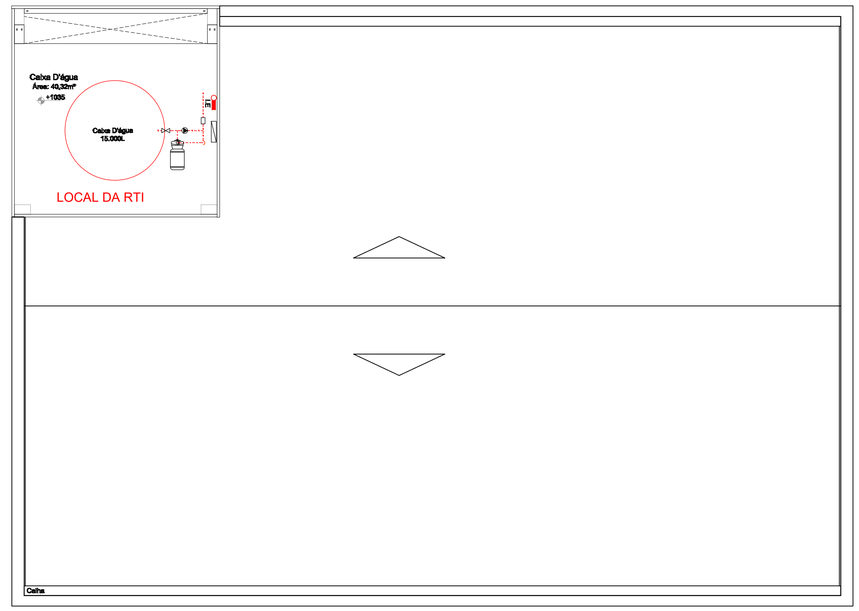


PLANTA DE COBERTURA

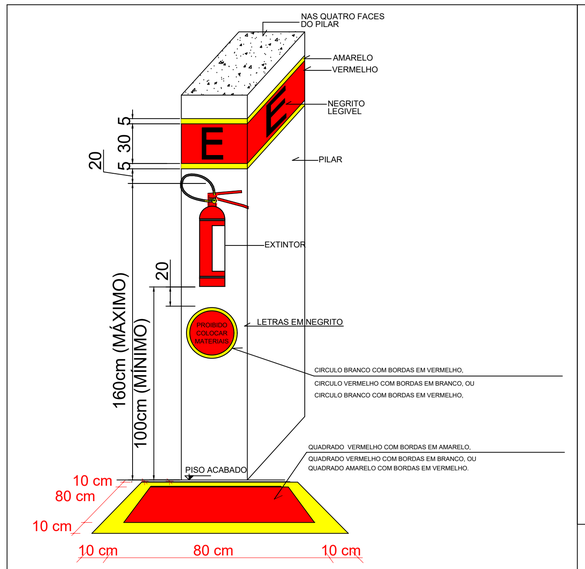


OBS.:
QUANDO INSTALADOS EM COLUNAS, PINTAR SOBRE OS EXTINTORES, COM FAIXA VERMELHA DE 20cm A 30cm E BORDAS DE 5cm EM AMARELO, A LETRA "E" NA COR PRETA EM TODAS AS FACES.

DETALHES DO EXTINTOR DE INCENDIO DE COLUNA

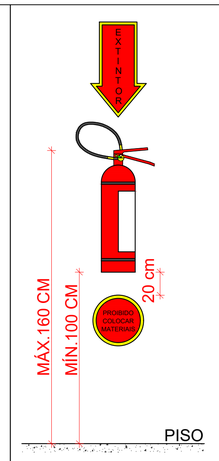


DETALHE EXTINTOR
ESC.: 1/50

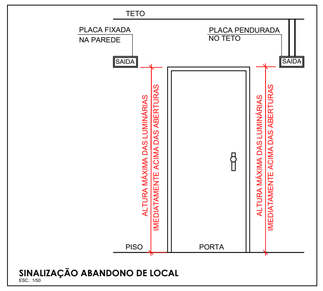

SINALIZAÇÃO ABANDONO DE LOCAL
ESC.: 1/50

FITA FOTOLUMINESCENTE

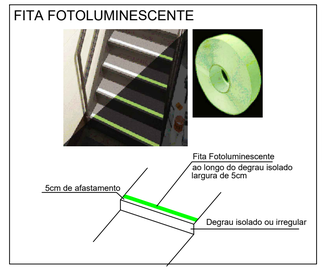


PLACA ADVERTÊNCIA DE DEGRAU IRREGULAR




A Sinalização para Abandono de Local está indicando todas as mudanças de direção, saídas, escadas, de tal forma que em cada ponto de sinalização seja possível visualizar o ponto seguinte.

A placa será fotoluminecente contendo, a mensagem "SAÍDA", possuindo fundo verde, ser de acrílico ou material similar, possuir seta direcional junto à mensagem "SAÍDA" (na mudança de direção).

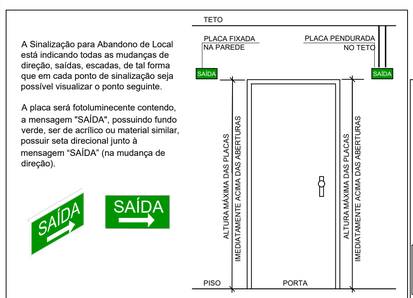

SINALIZAÇÃO DE ABANDONO DE LOCAL
TAMANHO DA PLACA INDICADO EM PROJETO

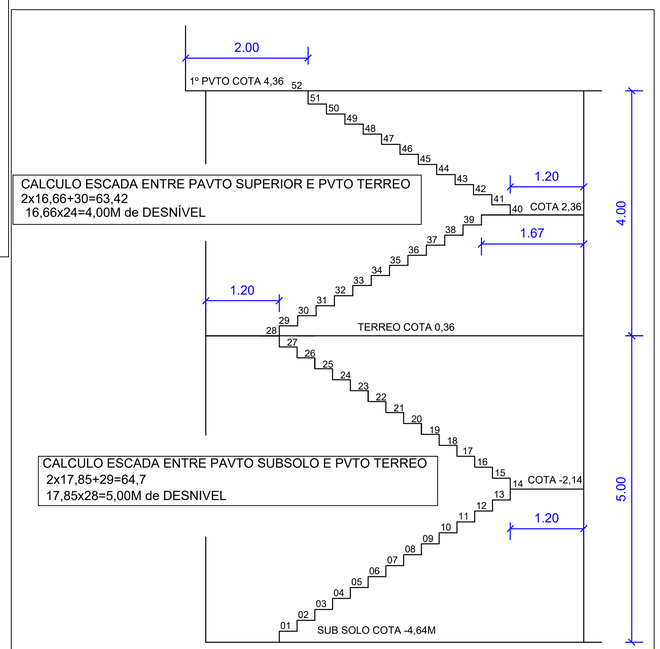



CALCULO ESCADA ENTRE PAVTO SUPERIOR E PVTO TERREO
2x16,66+30=63,42
16,66x24=4,00M de DESNÍVEL

CALCULO ESCADA ENTRE PAVTO SUBSOLO E PVTO TERREO
2x17,85+29=64,7
17,85x28=5,00M de DESNIVEL

DETALHE ESCADA EXTERNA

DIAGRAMA INSTALAÇÃO DO ACIONADOR

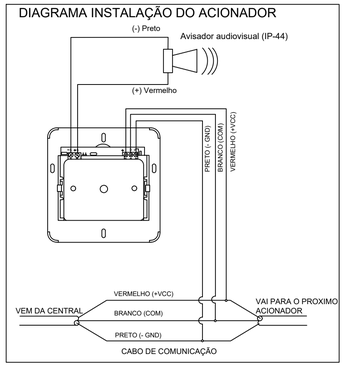

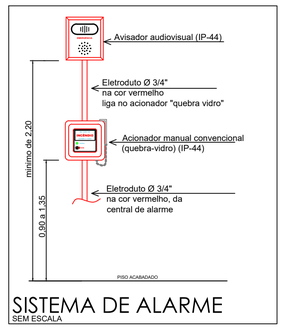

SISTEMA DE ALARME
SEM ESCALA

Central de Alarme Avalon L125A
Central 125 dispositivos endereçavel





Altura de instalação entre 1,40e 1,60m (no centro da central)

CARIMBOS:

ARIEL ANDRE MASSON
ENGENHEIRO CIVIL
CREA-SC 126637-3
47-988231636

PROPRIETÁRIO: Soeltech Desenvolvimento e Comércio de Sistemas Ltda
CNPJ: 80.090.244/0001-41

OBRA: EDIFICAÇÃO COM OCUPAÇÃO DE ESCRITÓRIO

ENDEREÇO: RUA DOS VEREADORES - BAIRRO ITOUPAVA - RIO DO SUL/SC

CONTEÚDO: PLANTA DE COBERTURA
DETALHES

DESENHO: LUCIANO R. KRUGER
ÁREA: 1.563,74 m²
ESCALA: 1/50
DATA: 05/05/2023
FOLHA: 05 05

RESPONSÁVEL TÉCNICO:
Assinado de forma digital por ARIEL ANDRE MASSON:09486173981
Dados: 2024.05.14 10:22:56 -03'00'
ARIEL ANDRÉ MASSON
CREA-SC: 126637-3

PROPRIETÁRIO:

PROJETO: PREVENTIVO

É vedada a reprodução e/ou utilização do projeto sem a autorização do autor Lei nº 5.988/73 - Direito Autoral